
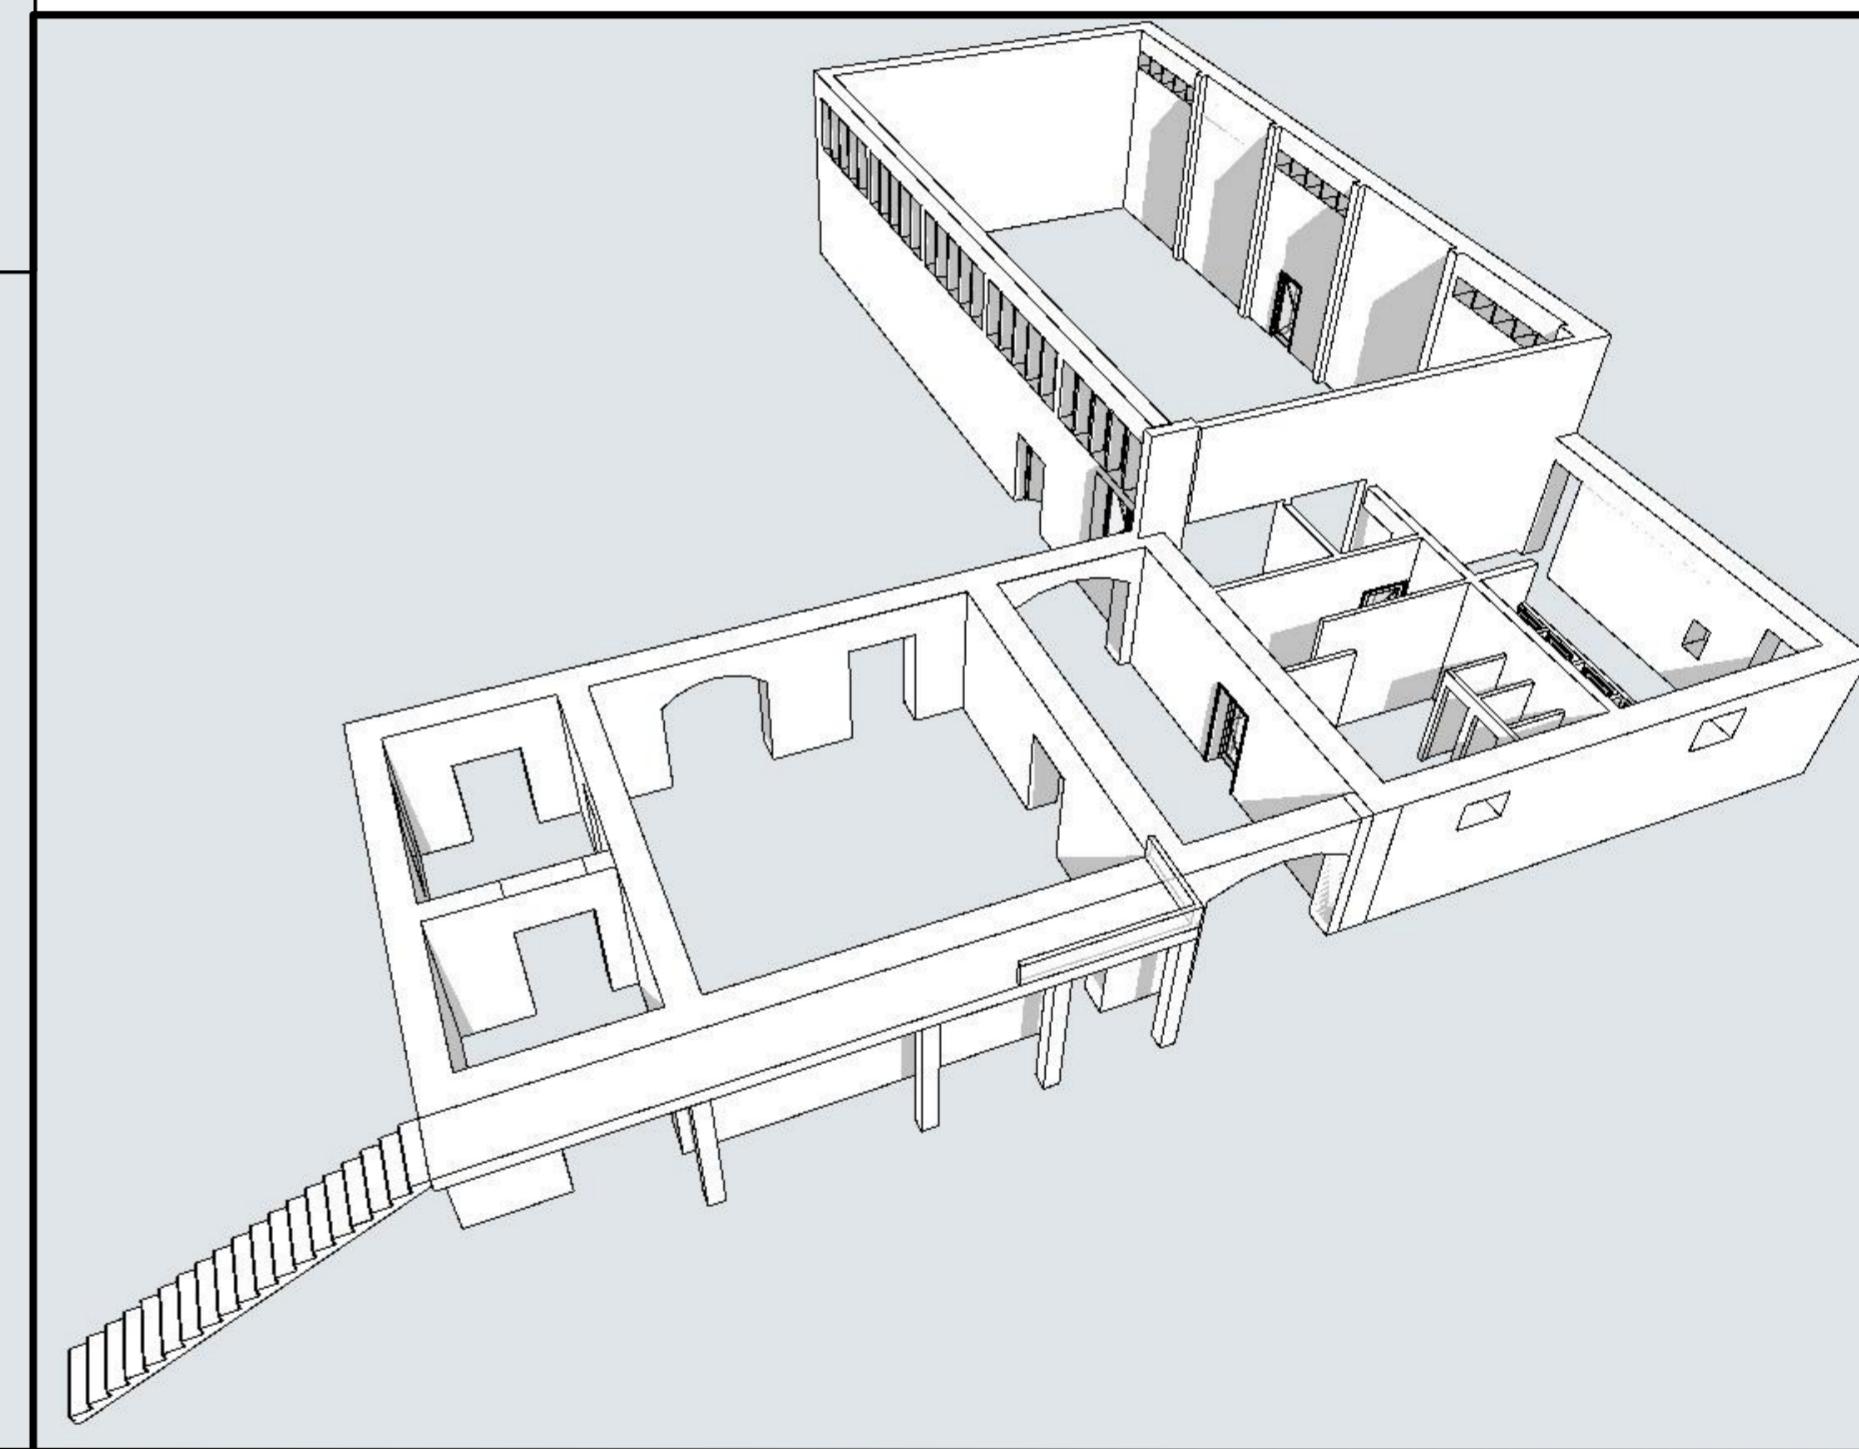
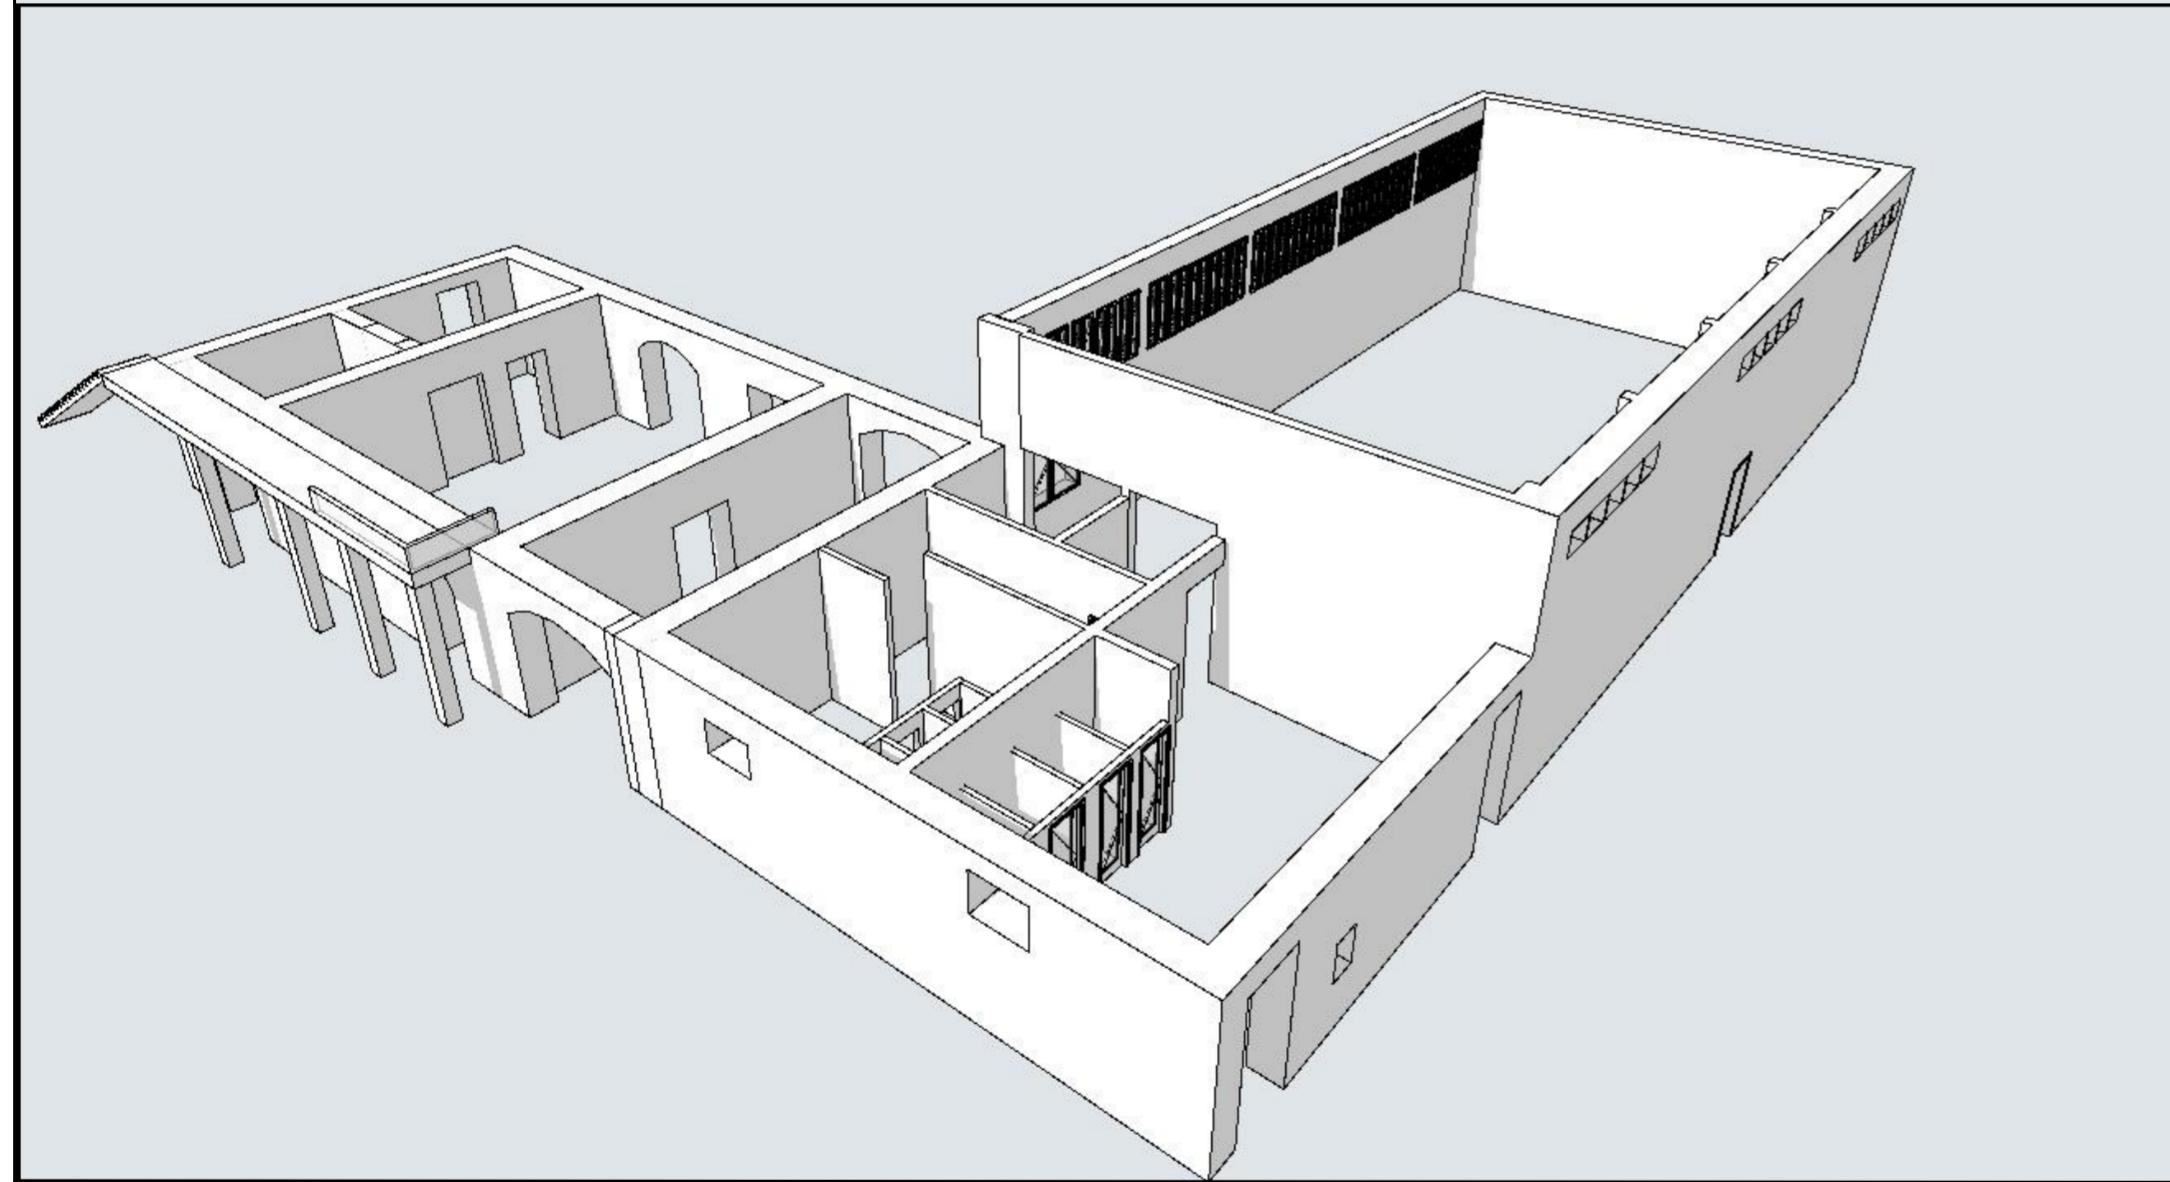


ОБЛЕНО

3D Floor plan

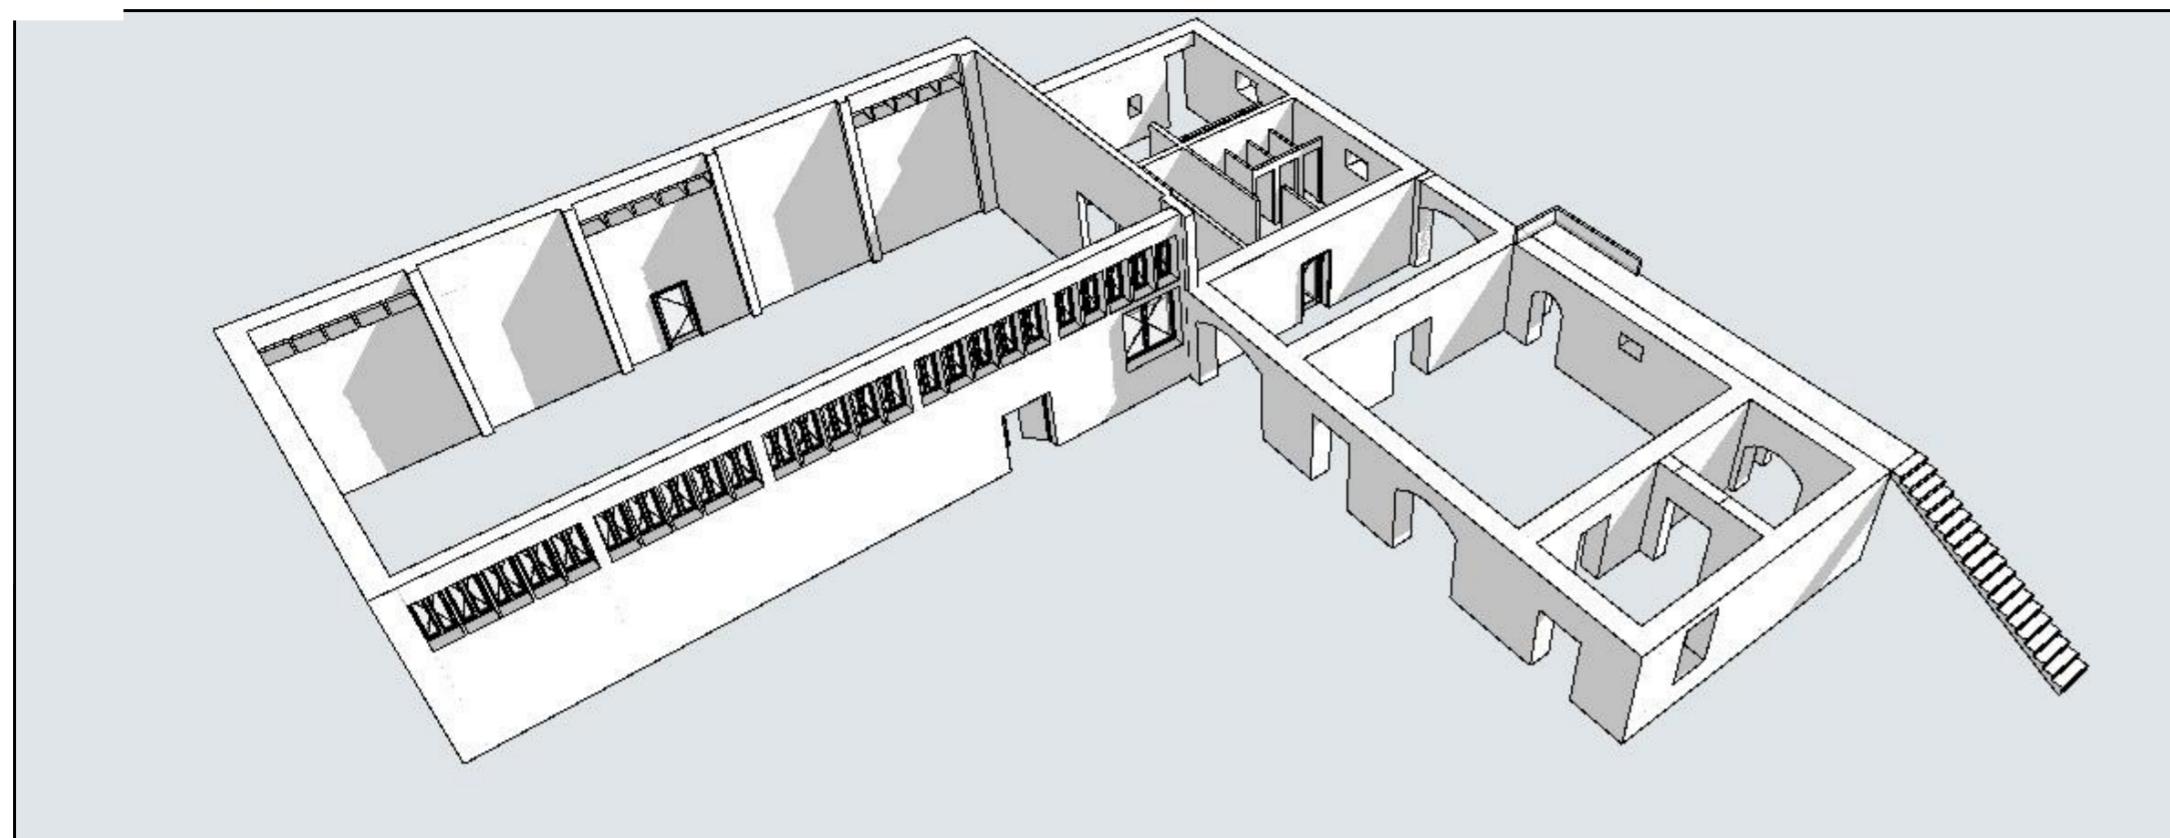

Примечание

Restaurant floor plan



Pula, Medulinska Cesta 173

3D план 1 этажа

Дата Лист Листов  
23.09.2024 1 3

## Экспликация помещений:

№	Найменование	Площадь, м <sup>2</sup>
1	Помещение №1	13,59
1.1	Помещение №1.1	9,99
2	Помещение №2	60,25
3	Помещение №3	26,29
4	Помещение №4	25,25
4.1	Санузел	3,44
5	Помещение №5	7,57
6	Помещение №6	32,80
6.1	Санузел	5,53
7	Помещение №7	4,17
8	Помещение №8	6,24
9	Помещение №9	206,99
10	Терраса	219,64
11	Терраса	101,05
		722,08

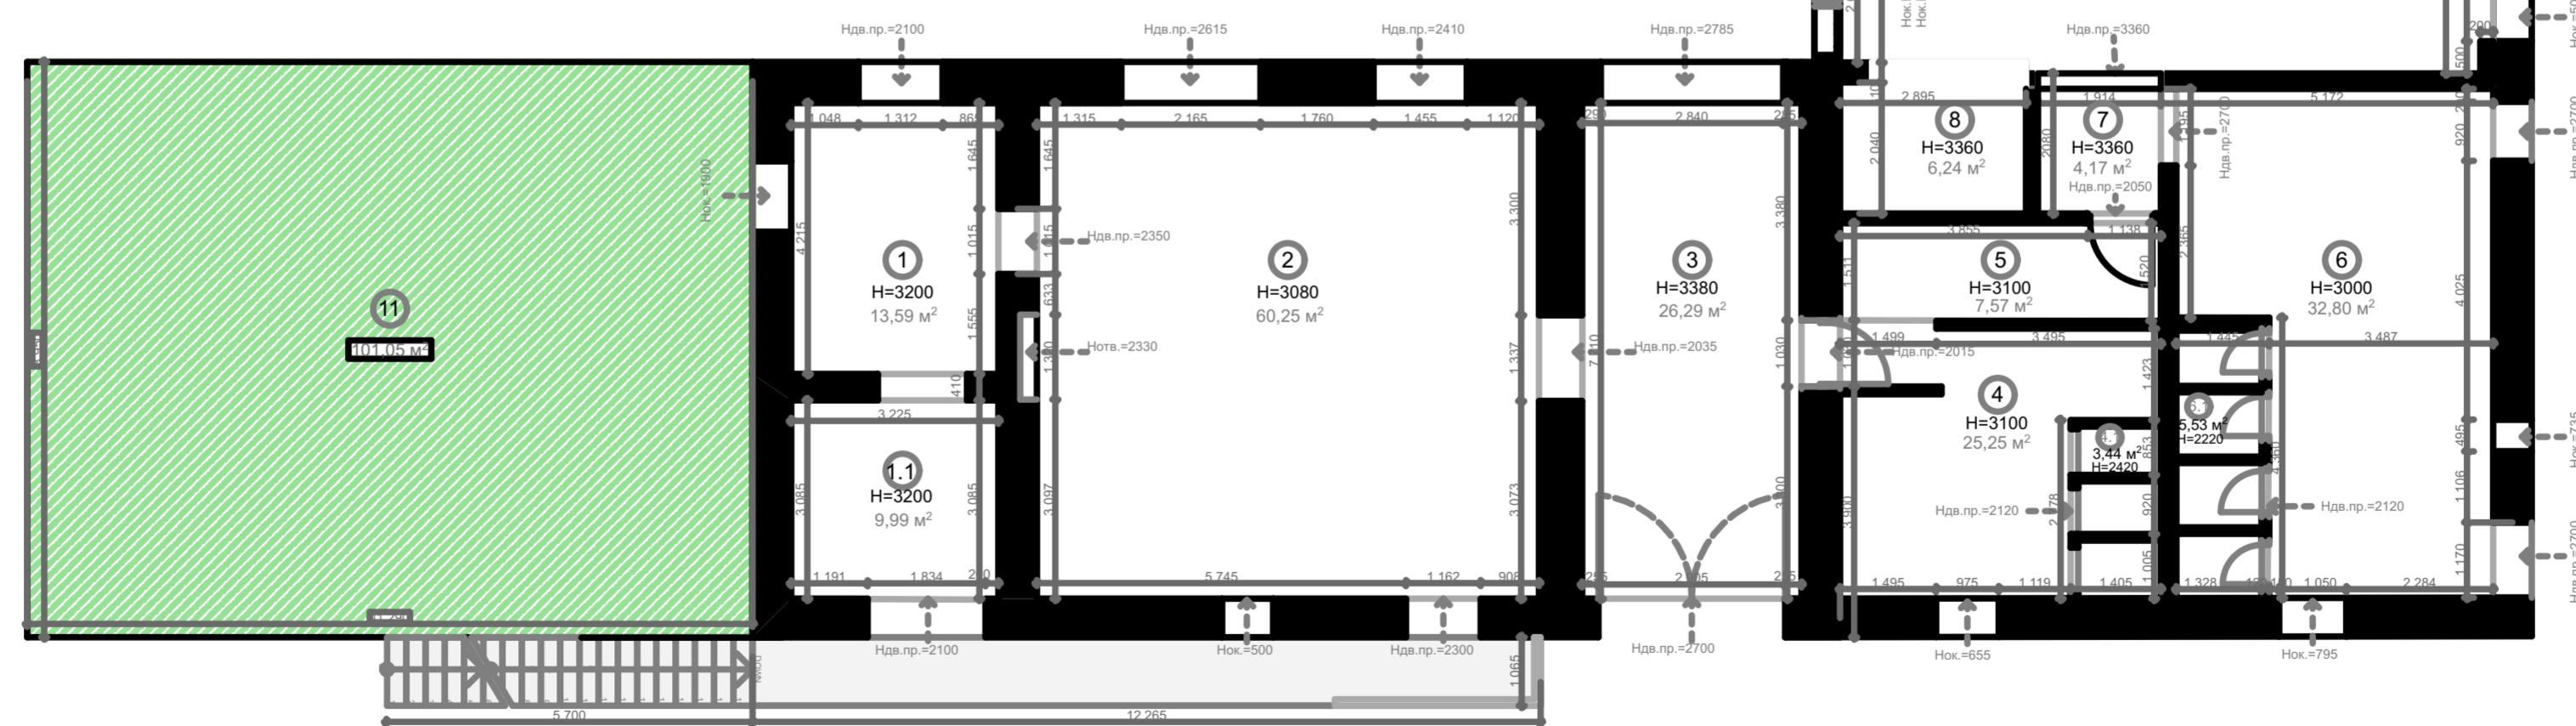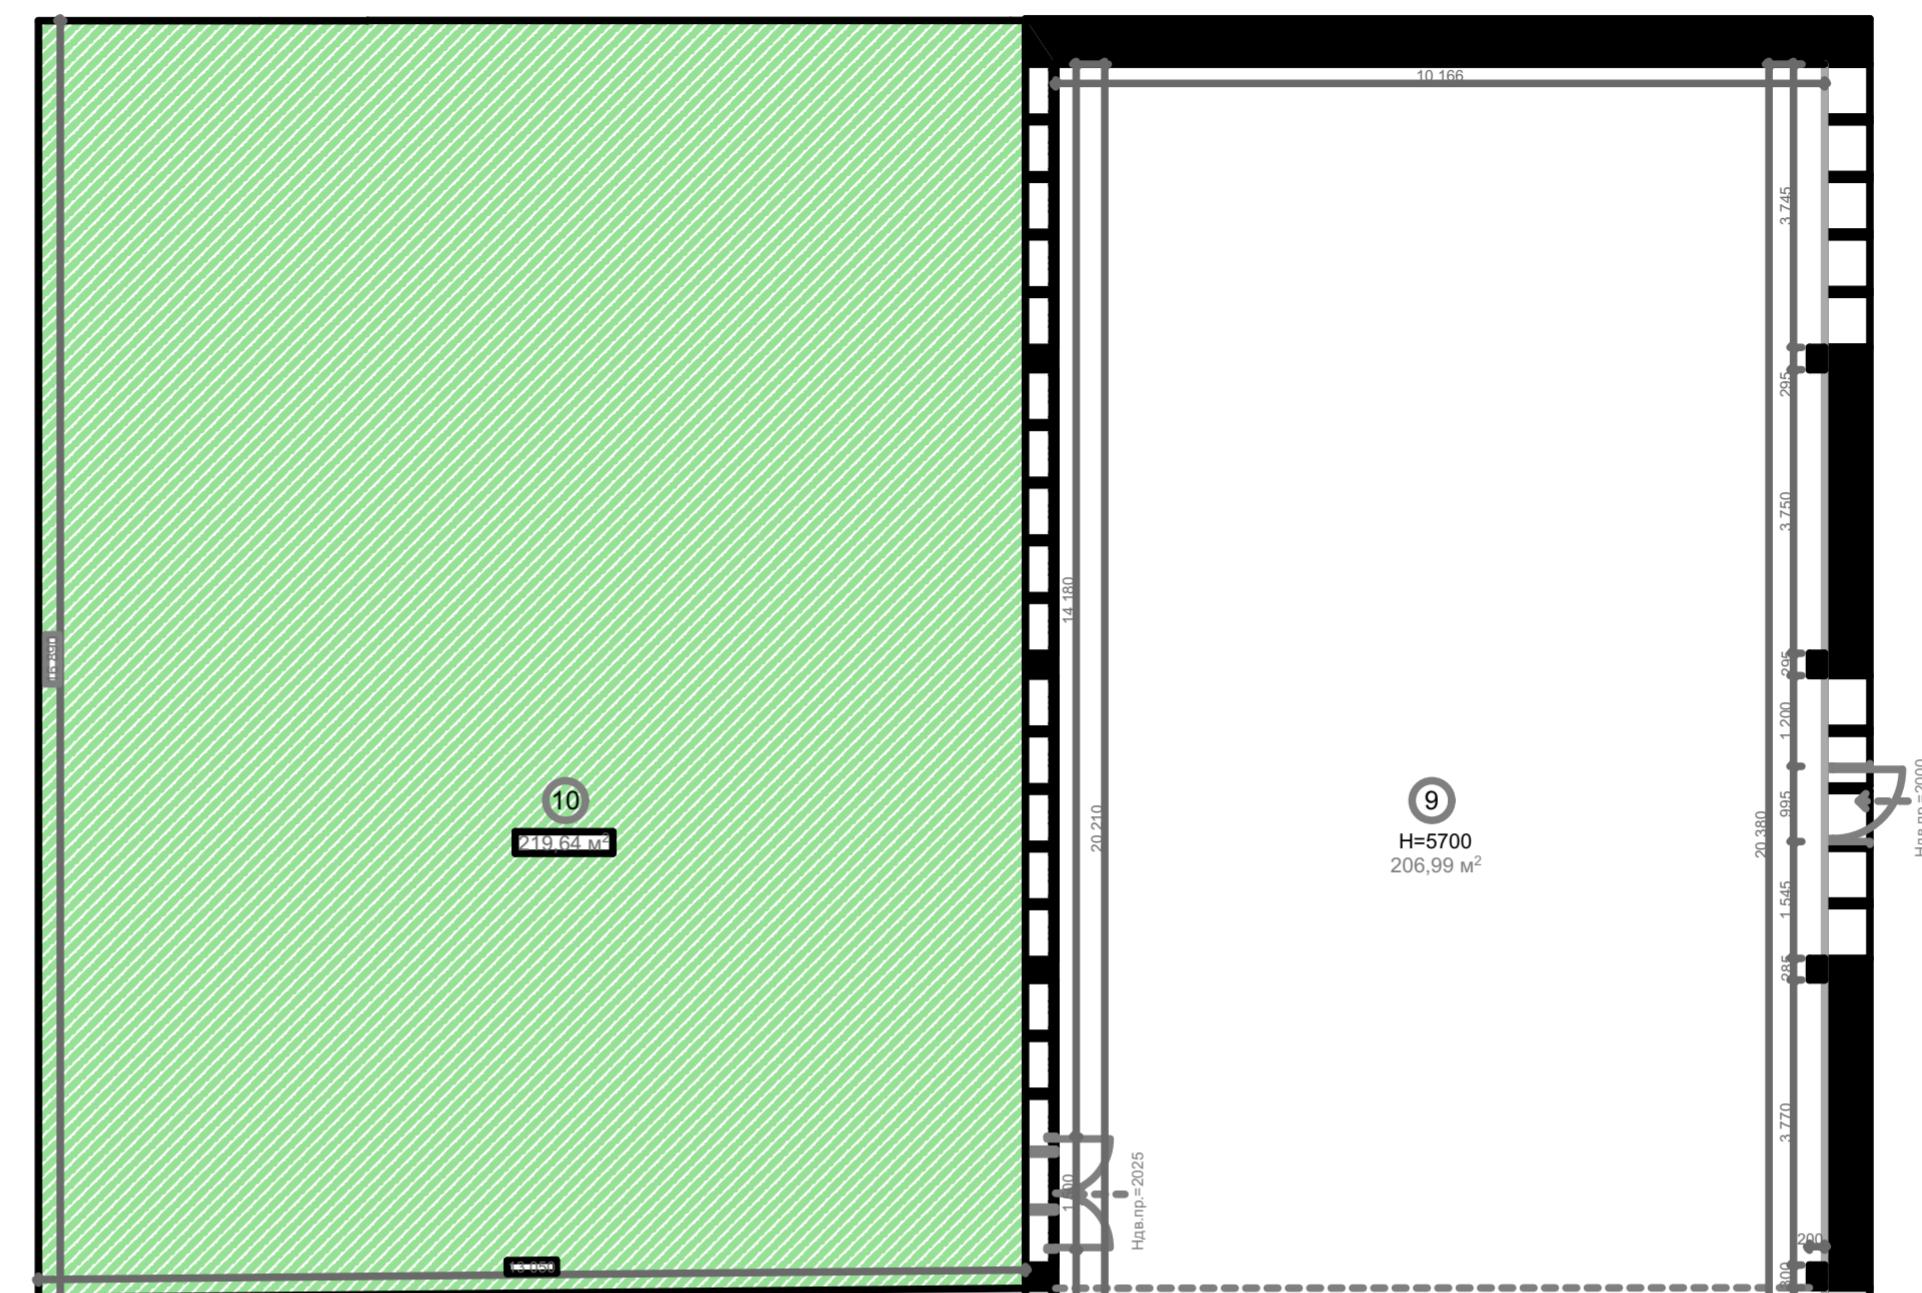

## Примечание

\*Все размеры указаны в мм

Общая площадь 722,08 м<sup>2</sup>

## Restaurant floor plan



Pula, Medulinska Cesta 173

Обмерочный чертеж 1 этажа

Дата	Лист	Листов
23.09.2024	2	3

## Экспликация помещений:

№	Найменование	Площадь, м <sup>2</sup>
12	Помещение №12	24,74
13	Помещение №13	60,29
14	Помещение №14	26,19
15	Помещение №15	53,05
15.1	Помещение №15.1	8,39
15.2	Помещение №15.2	18,08
		190,74

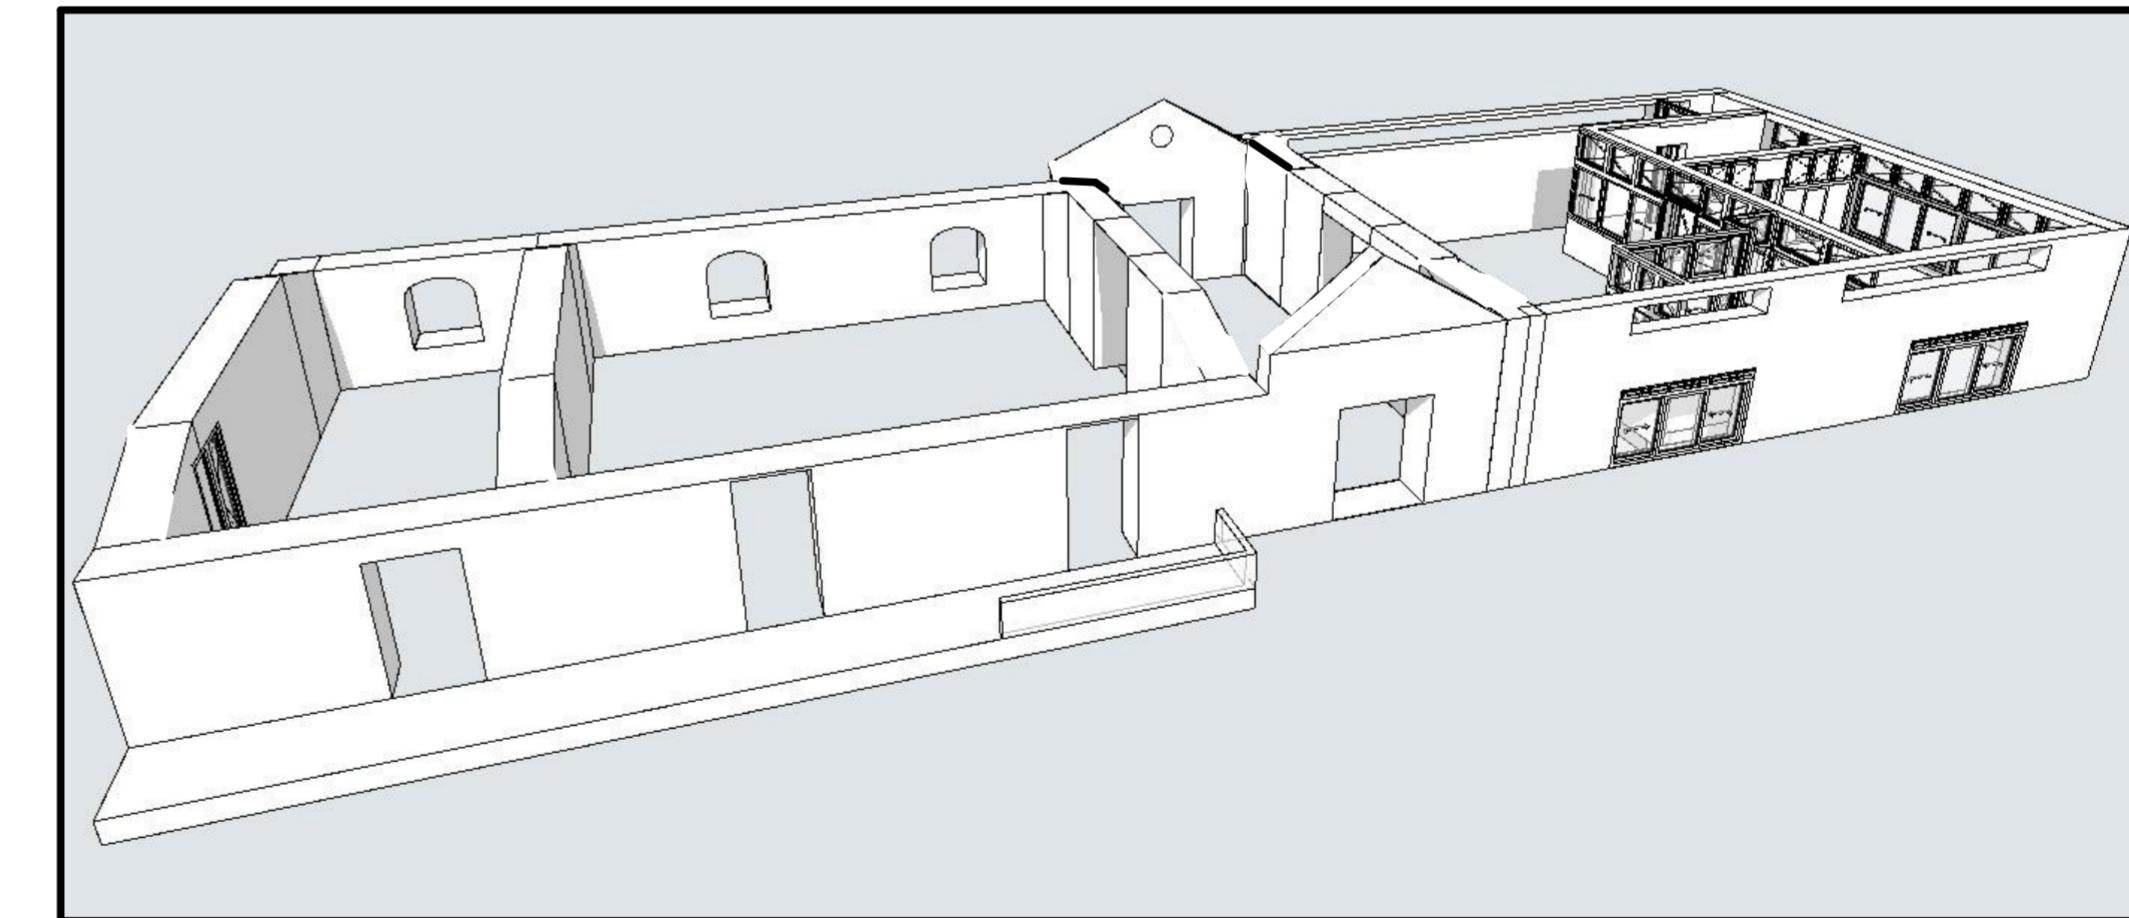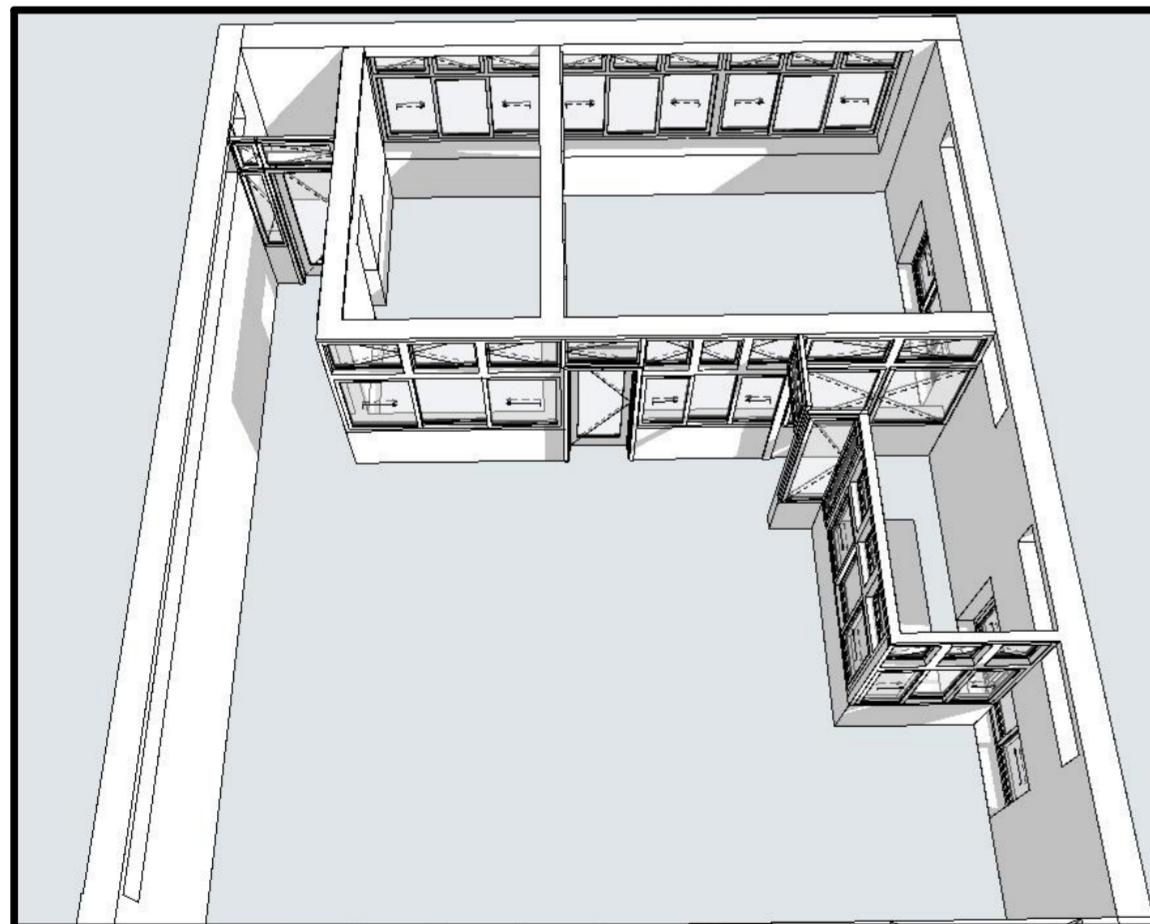

Примечание

\*Все размеры указаны в мм  
Общая площадь 190,74 м<sup>2</sup>

Restaurant floor plan

Pula, Medulinska Cesta 173

Обмерочный чертеж 2 этажа

Дата Лист Листов

23.09.2024 3 3